

Architecture
 Engineering
 Construction Management
 Planning
 Interiors

Project MFL No.: 2951.00


Nā Hale o Makena
 FIRST AMENDED
 CONDOMINIUM MAP

Keyplan


No.	Rev.	Date	Description

Consultant

Project Director: MC
 Project Architect: GR
 Drawn By: V.H., AP, WL
 Checked By: GR
 Date: 7/5/01

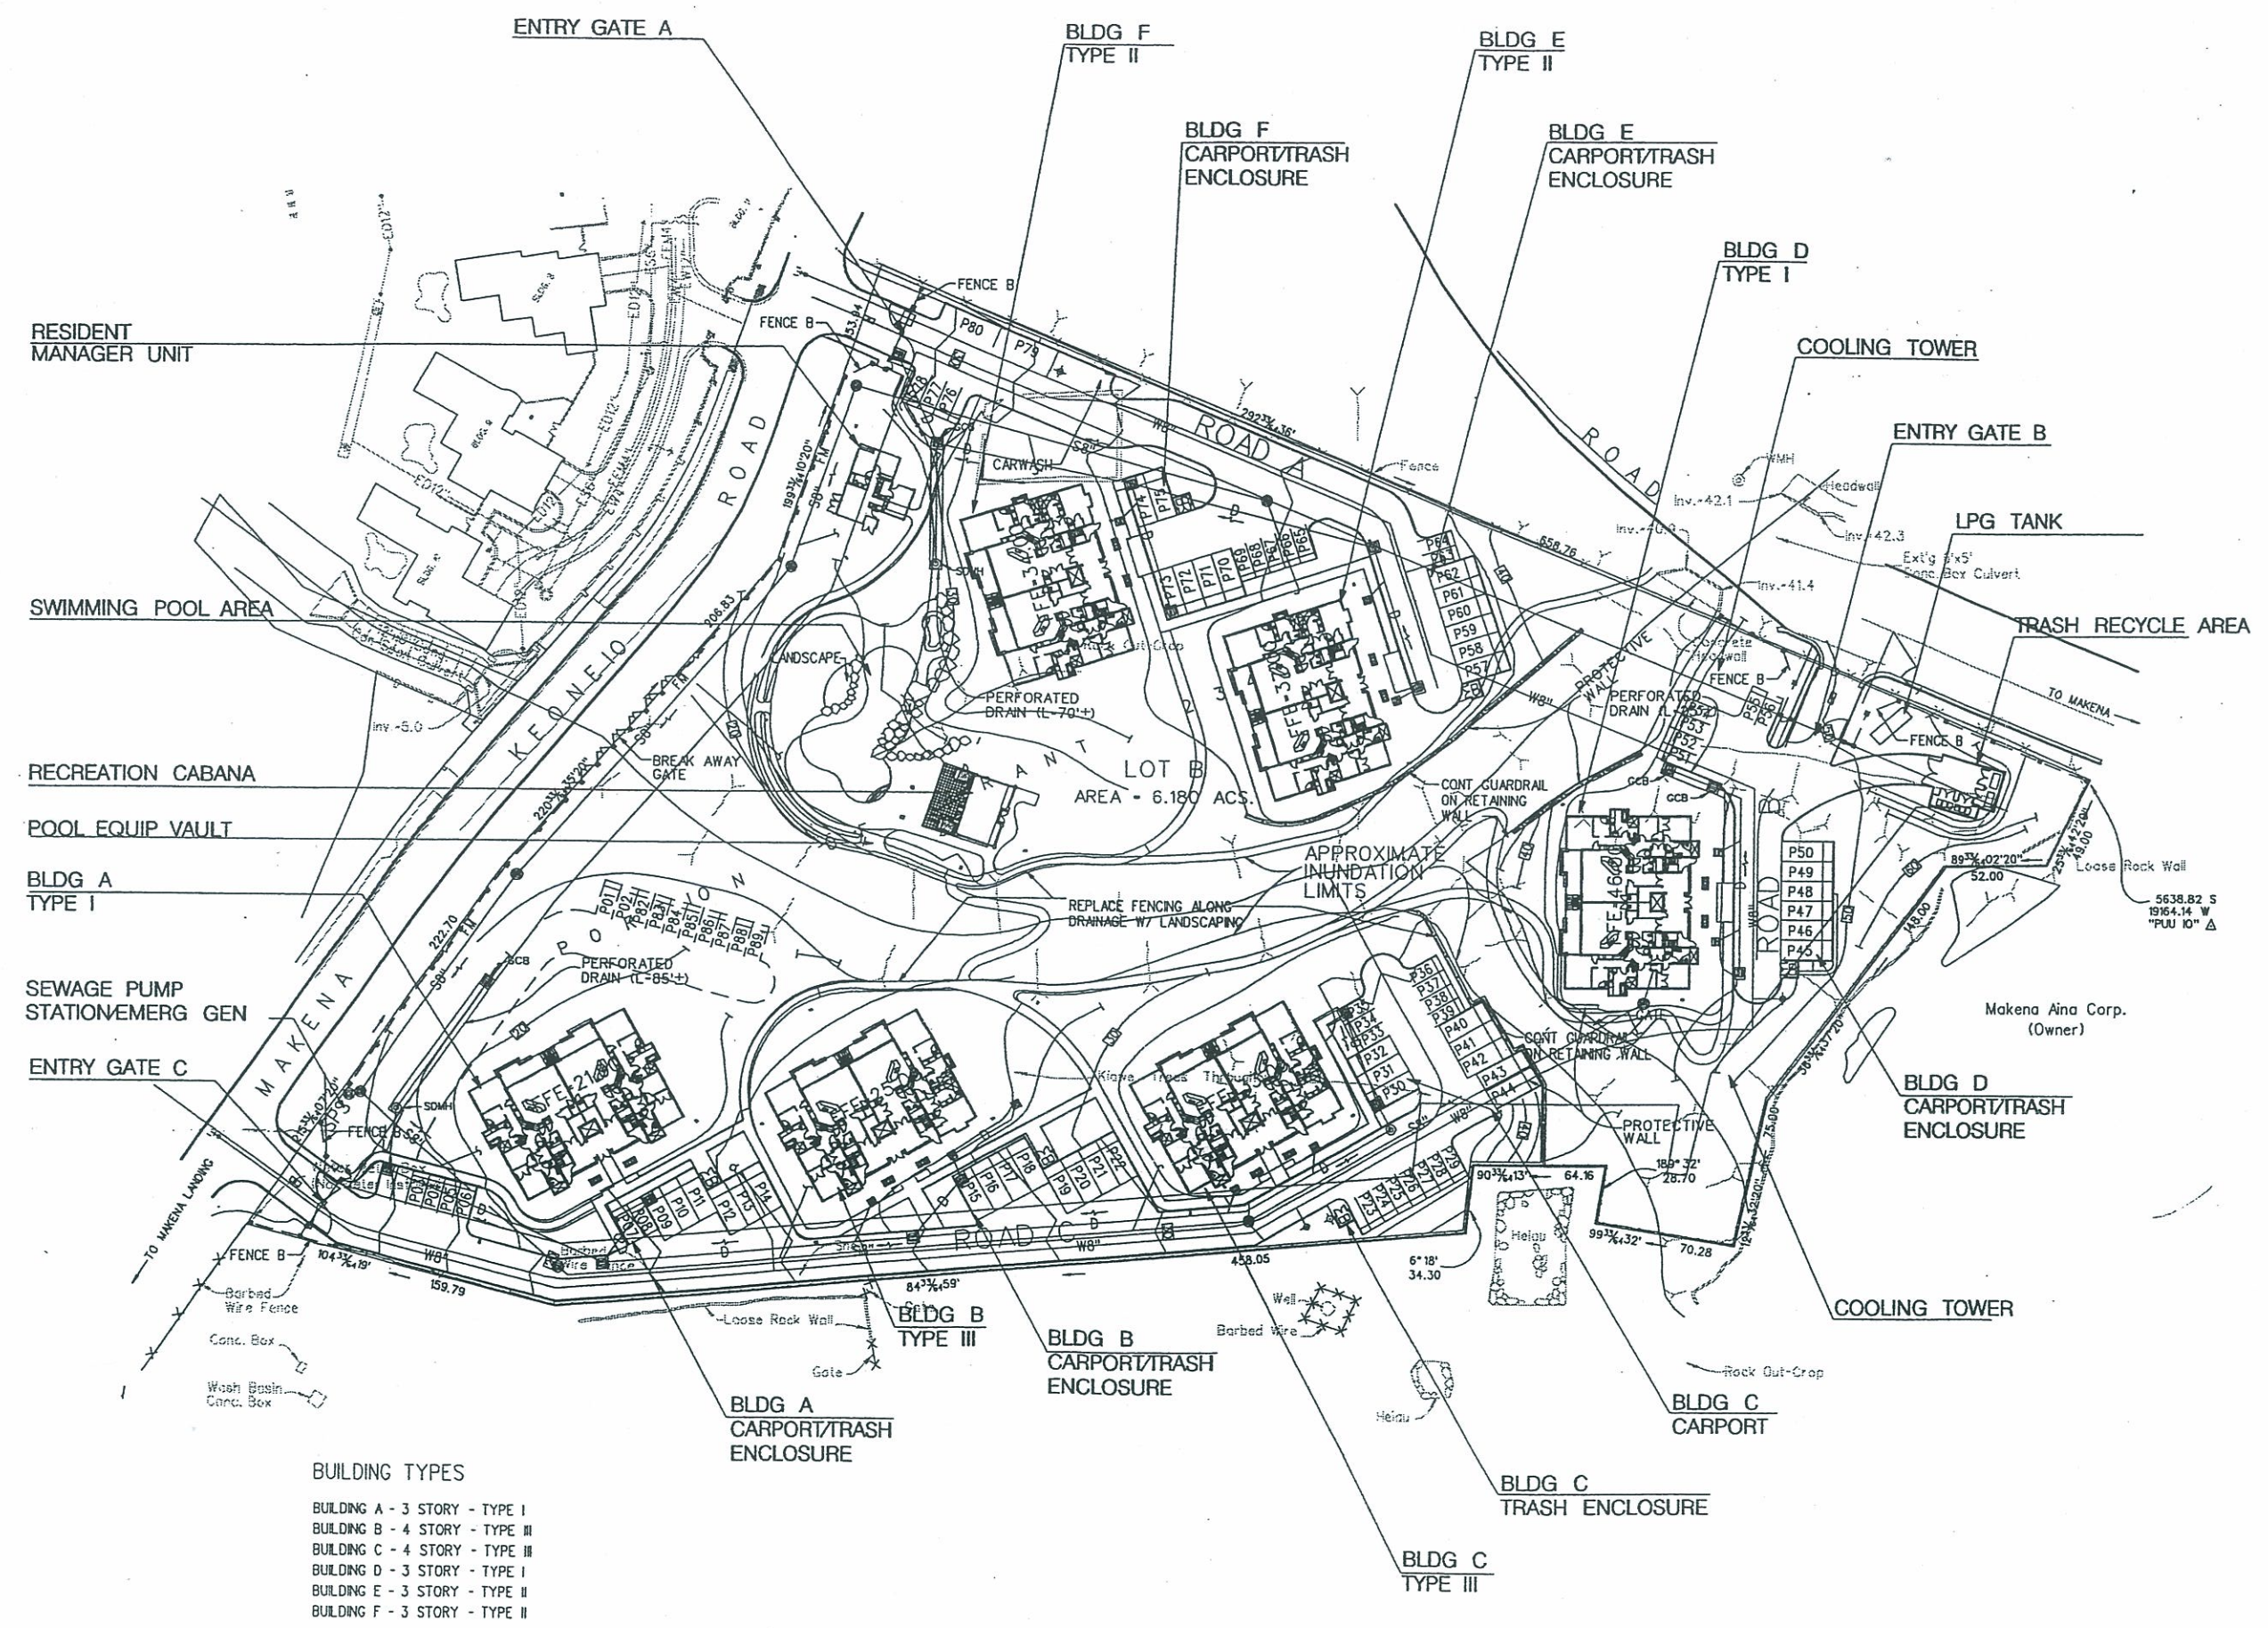


- BUILDING TYPES**
- BUILDING A - 3 STORY - TYPE I
 - BUILDING B - 4 STORY - TYPE III
 - BUILDING C - 4 STORY - TYPE III
 - BUILDING D - 3 STORY - TYPE I
 - BUILDING E - 3 STORY - TYPE II
 - BUILDING F - 3 STORY - TYPE II

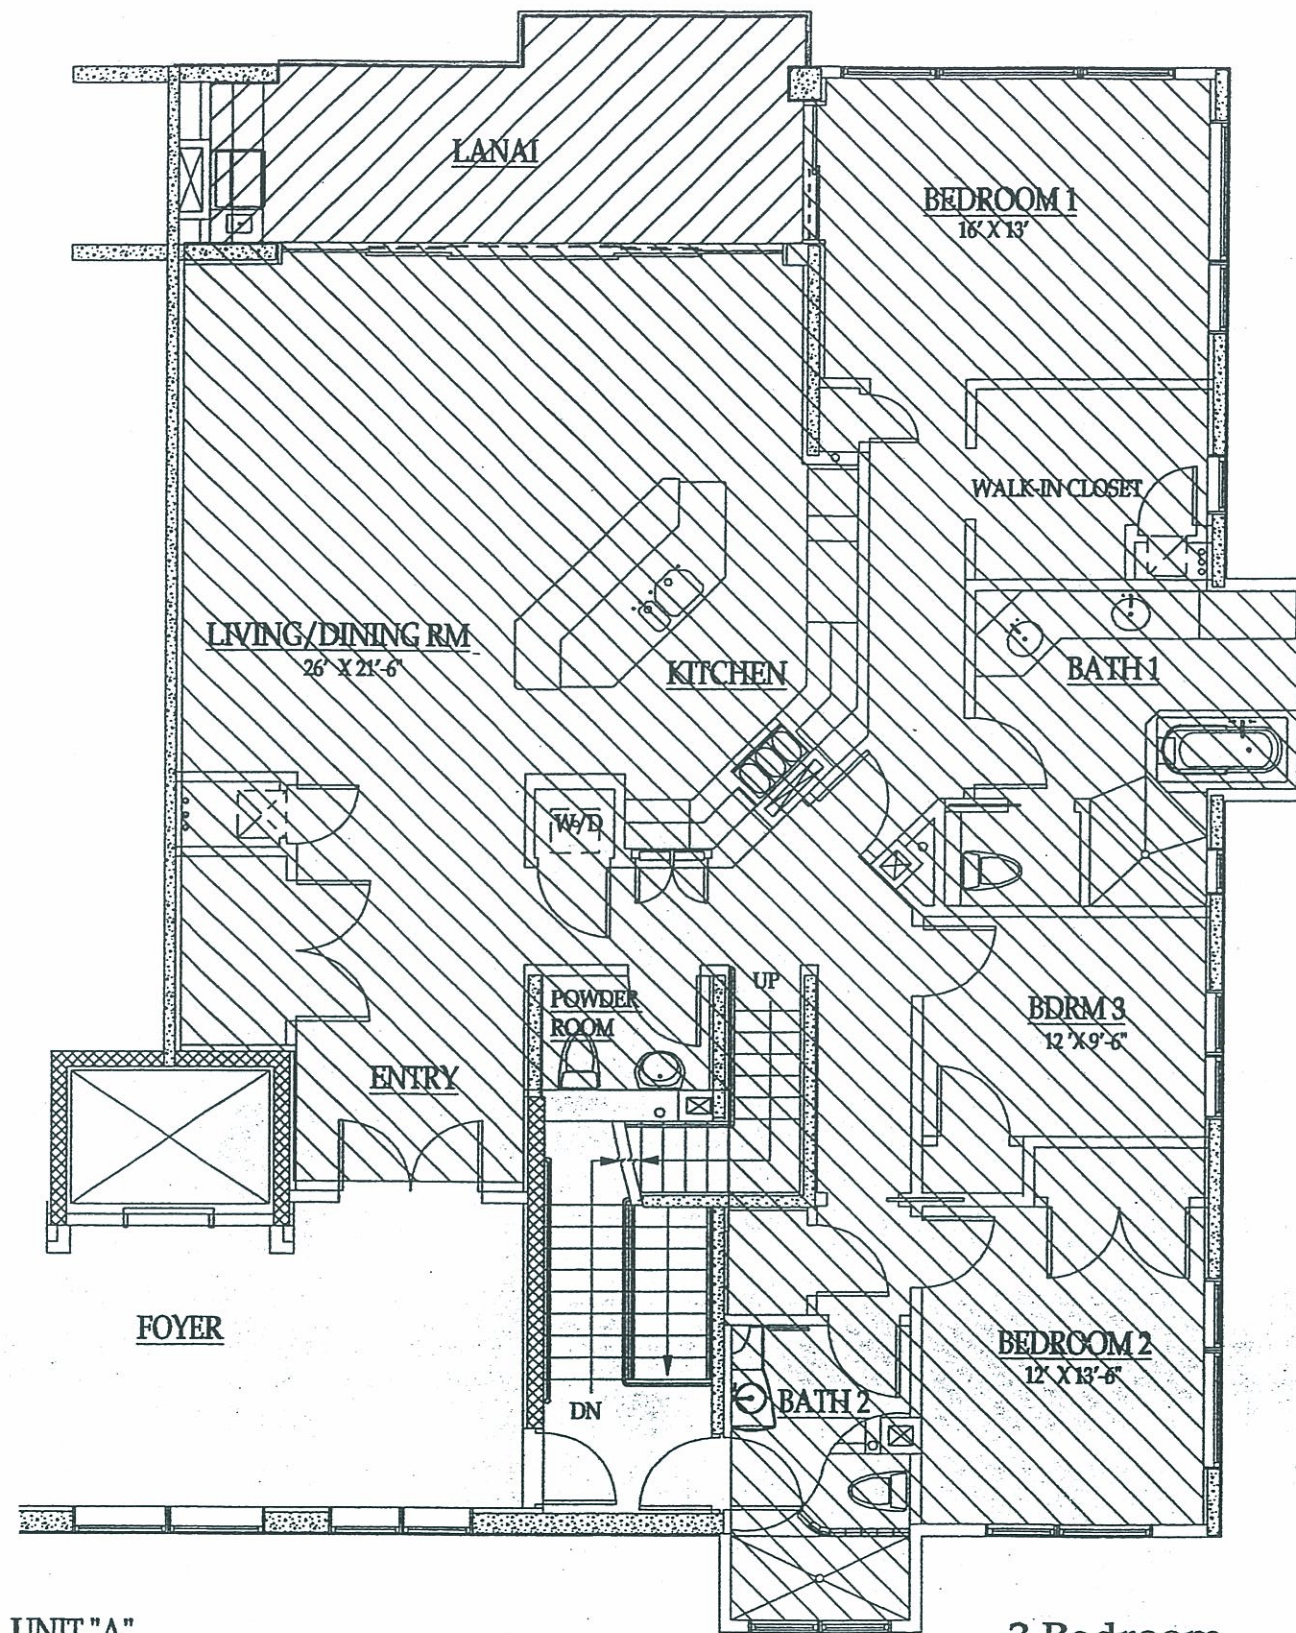

UNIT "A"

NET LIVING AREA: 2116 SF
NET LANAI AREA: 206 SF

3 Bedroom
Top Floor
SCALE: 1/8" = 1'-0"

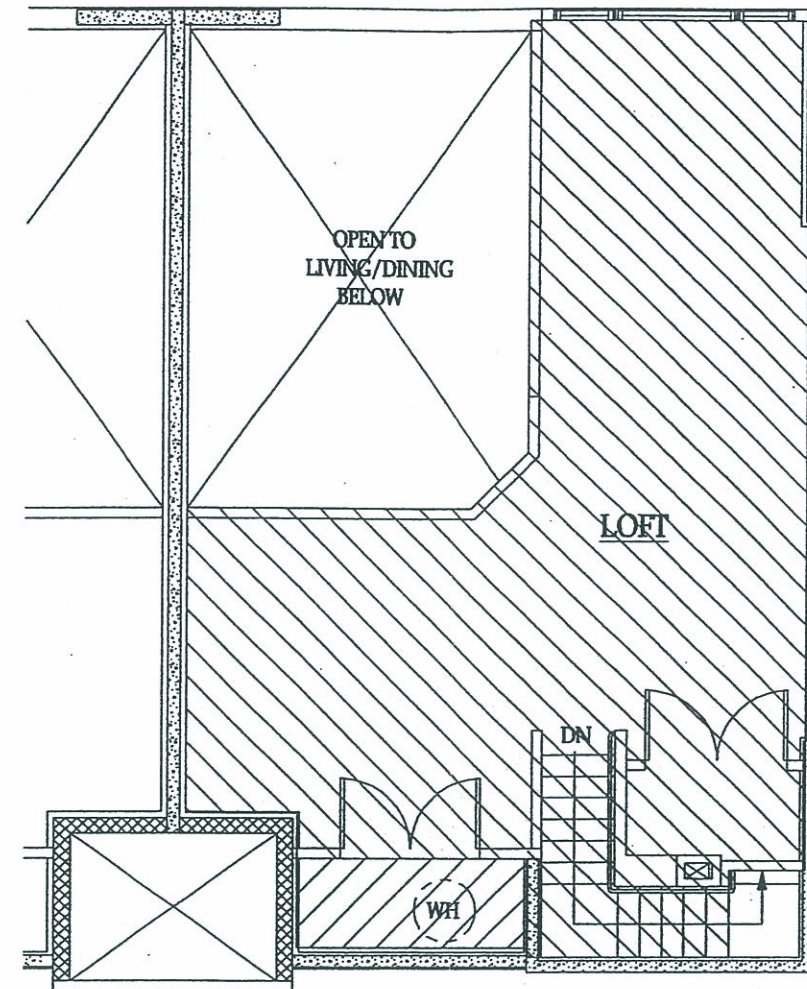


UNIT "A"

NET LOFT AREA: 657 SF

LOFT

SCALE: 1/8" = 1'-0"

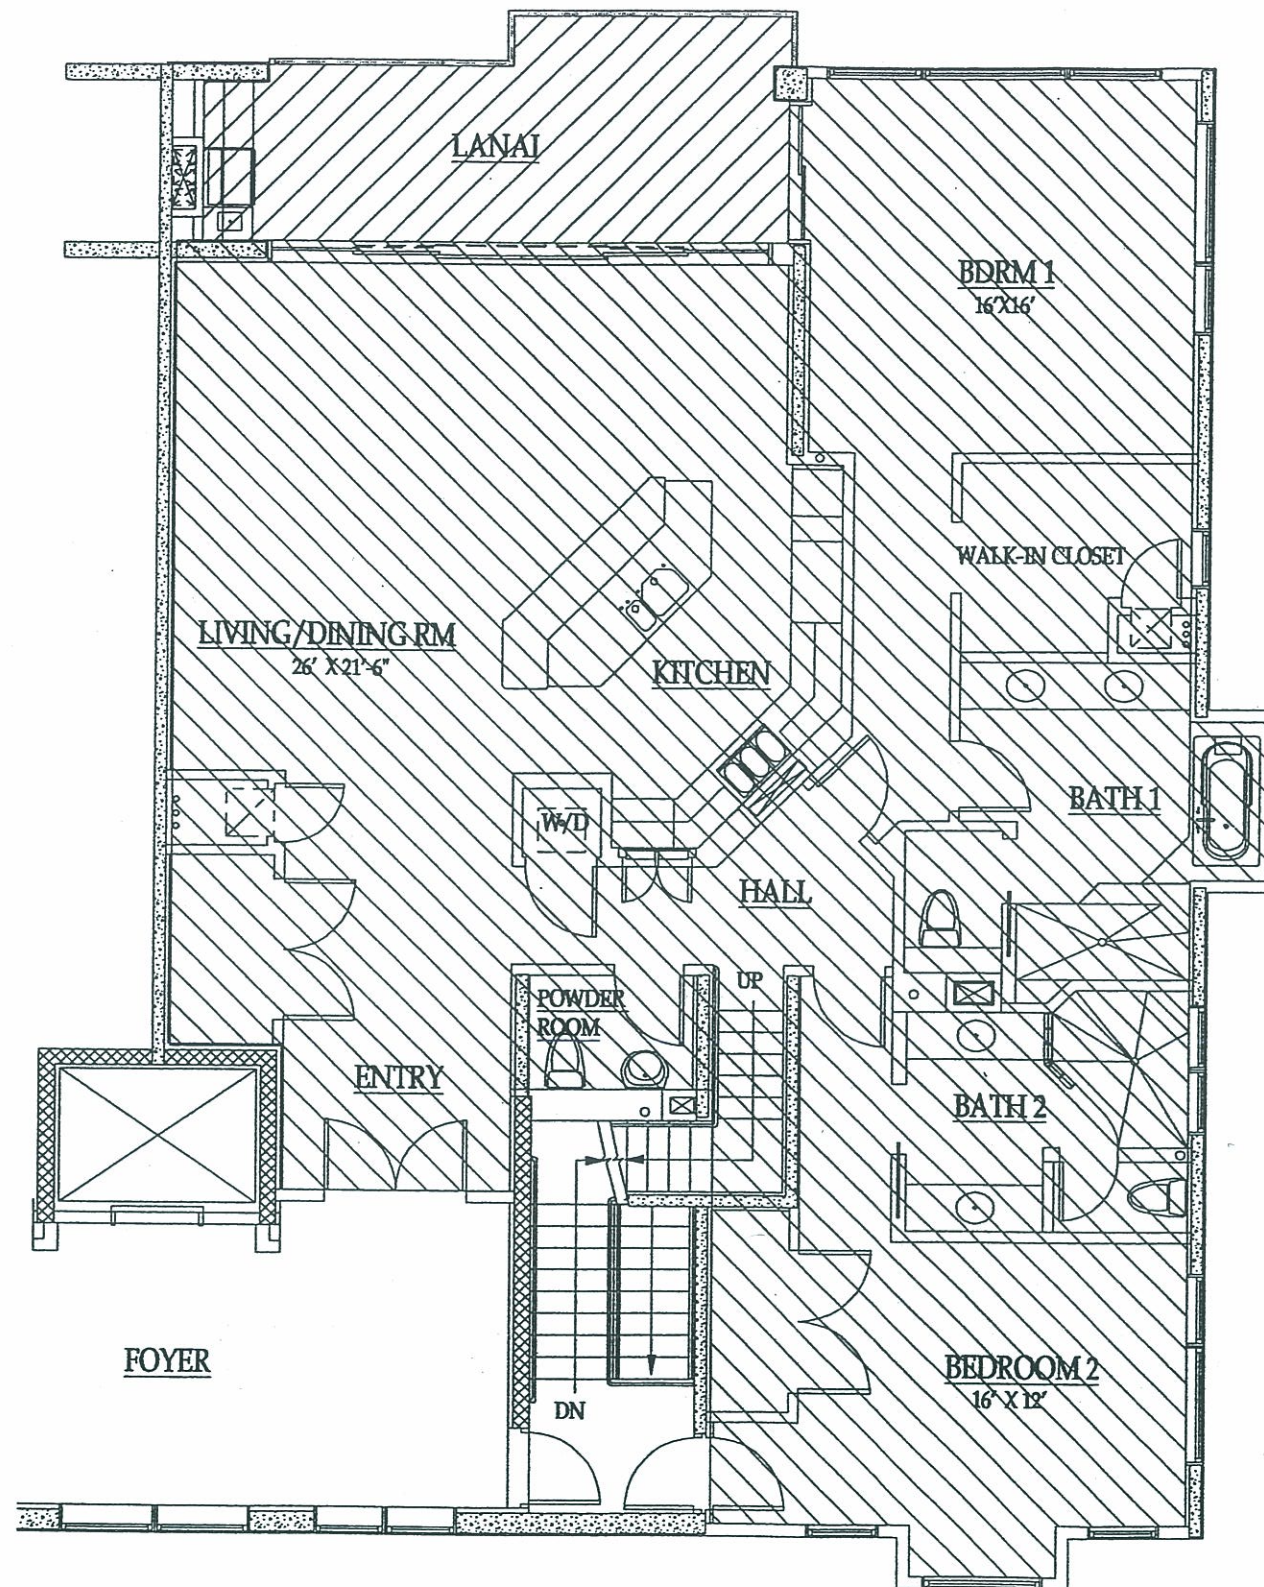


UNIT "B"

NET LIVING AREA: 2088 SF
NET LANAI AREA: 206 SF

**2 Bedroom
Top Floor**

SCALE: 1/8" = 1'-0"

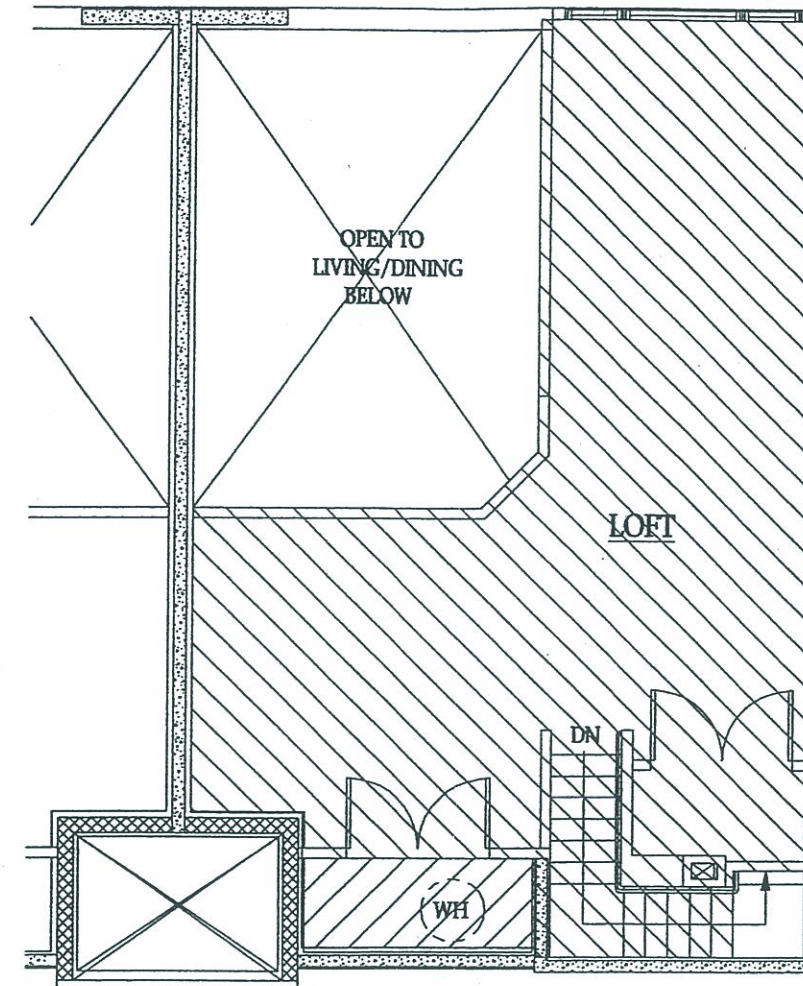

UNIT "B"

NET LOFT AREA: 657 SF

LOFT


SCALE: 1/8" = 1'-0"

Makena Estates, LLC



FIRST AMENDED CONDOMINIUM MAP

Nā Hale Mākena
M ā k e n a , M a u i , H a w a i ' i

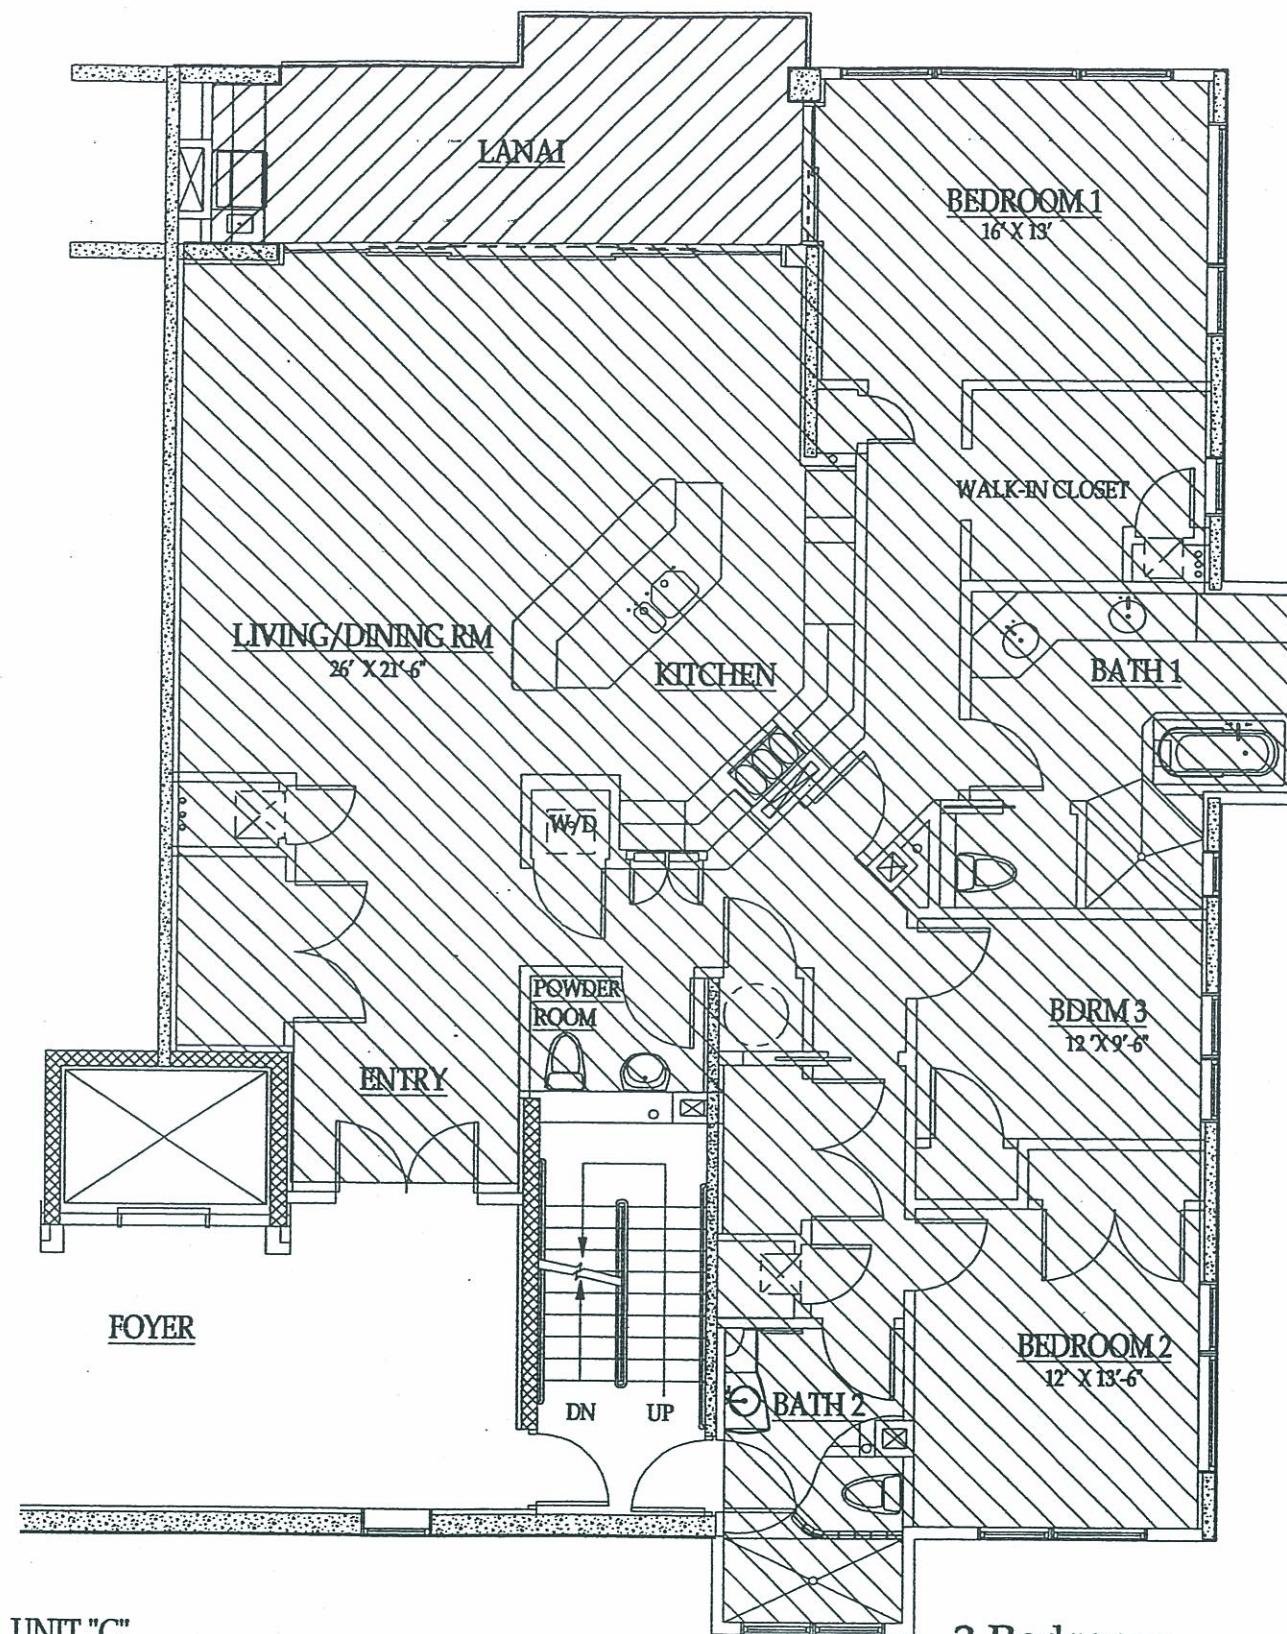

UNIT "C"

NET LIVING AREA: 2116 SF

NET LANAI AREA: 206 SF

3 Bedroom
Middle Floor


SCALE: 1/8" = 1'-0"

FIRST AMENDED CONDOMINIUM MAP

Makena Estates, LLC



Nā Hale  Mākena
M ā k e n a, M a u i, H a w a i ' i

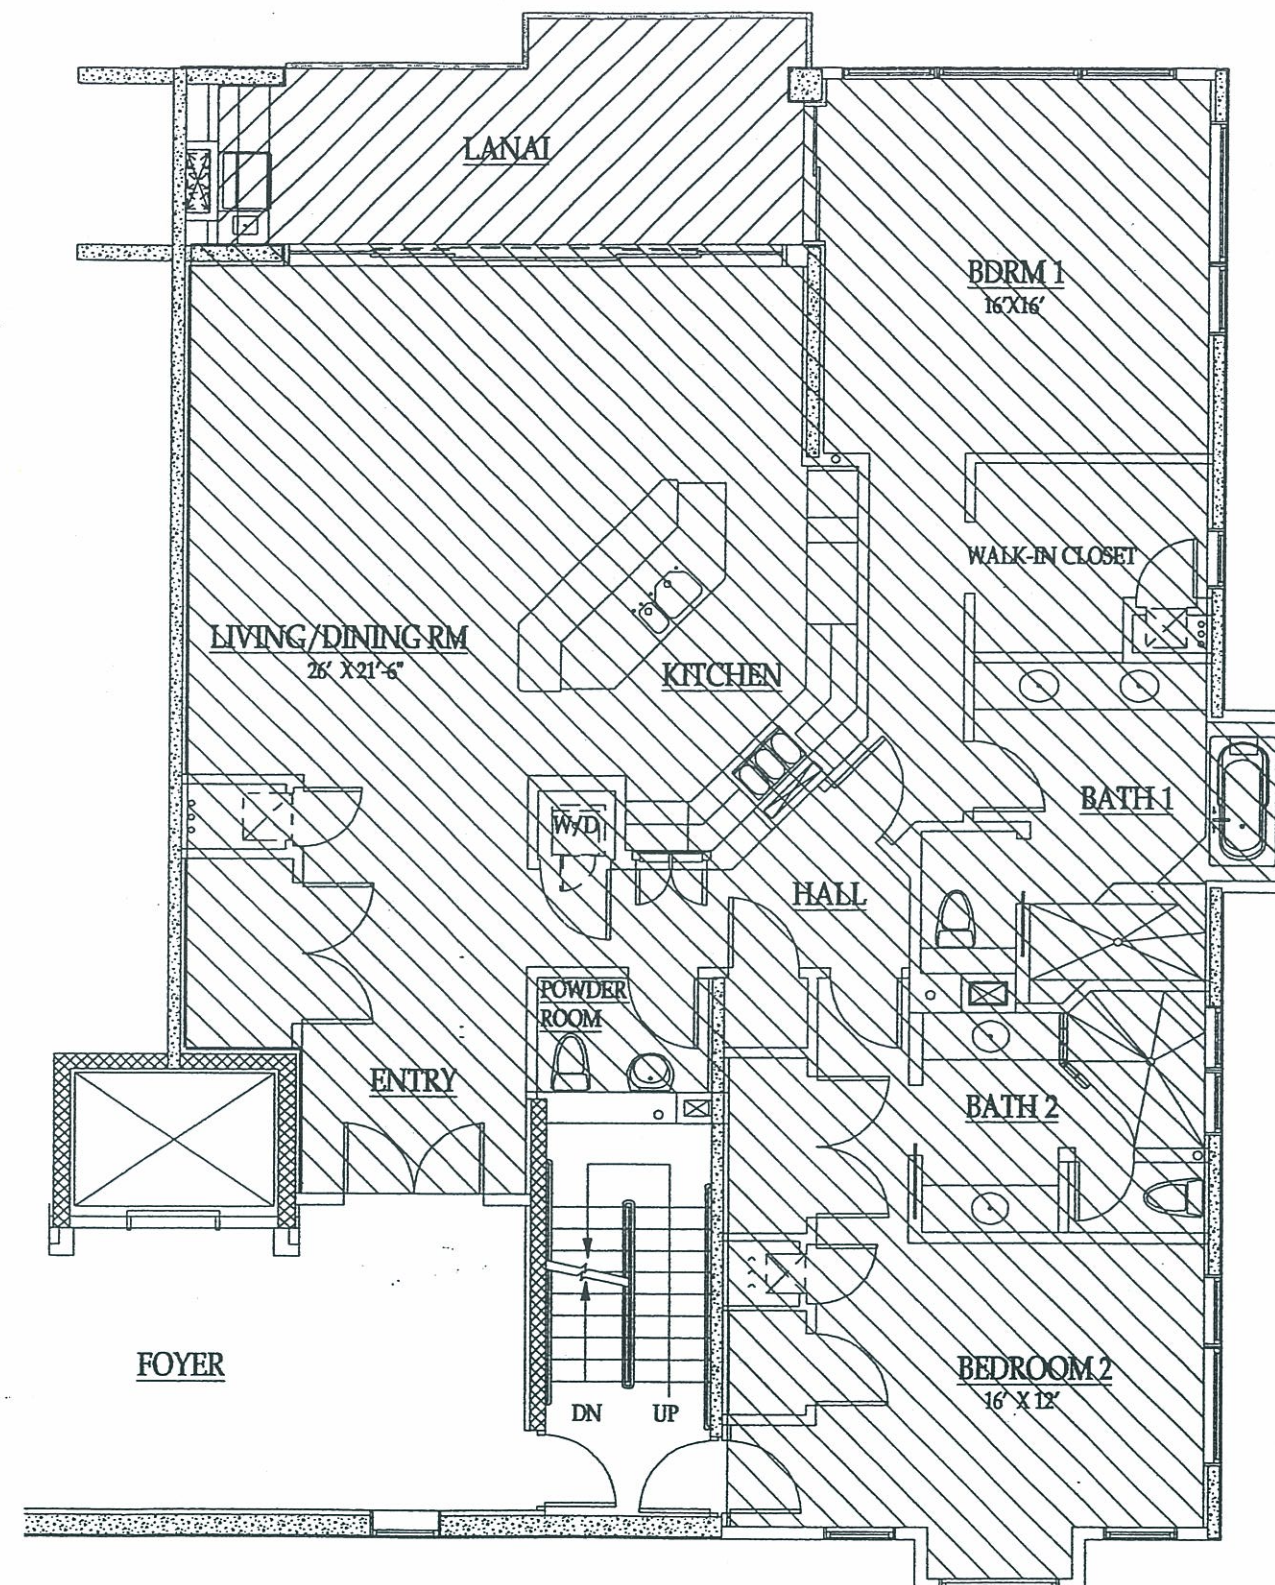

UNIT "D"

NET LIVING AREA: 2088 SF

NET LANAI AREA: 206 SF

2 Bedroom
Middle Floor


SCALE: 1/8" = 1'-0"

Makena Estates, LLC



FIRST AMENDED CONDOMINIUM MAP

Nā Hale  Mākena
M ā k e n a , M a u i , H a w a i ' i

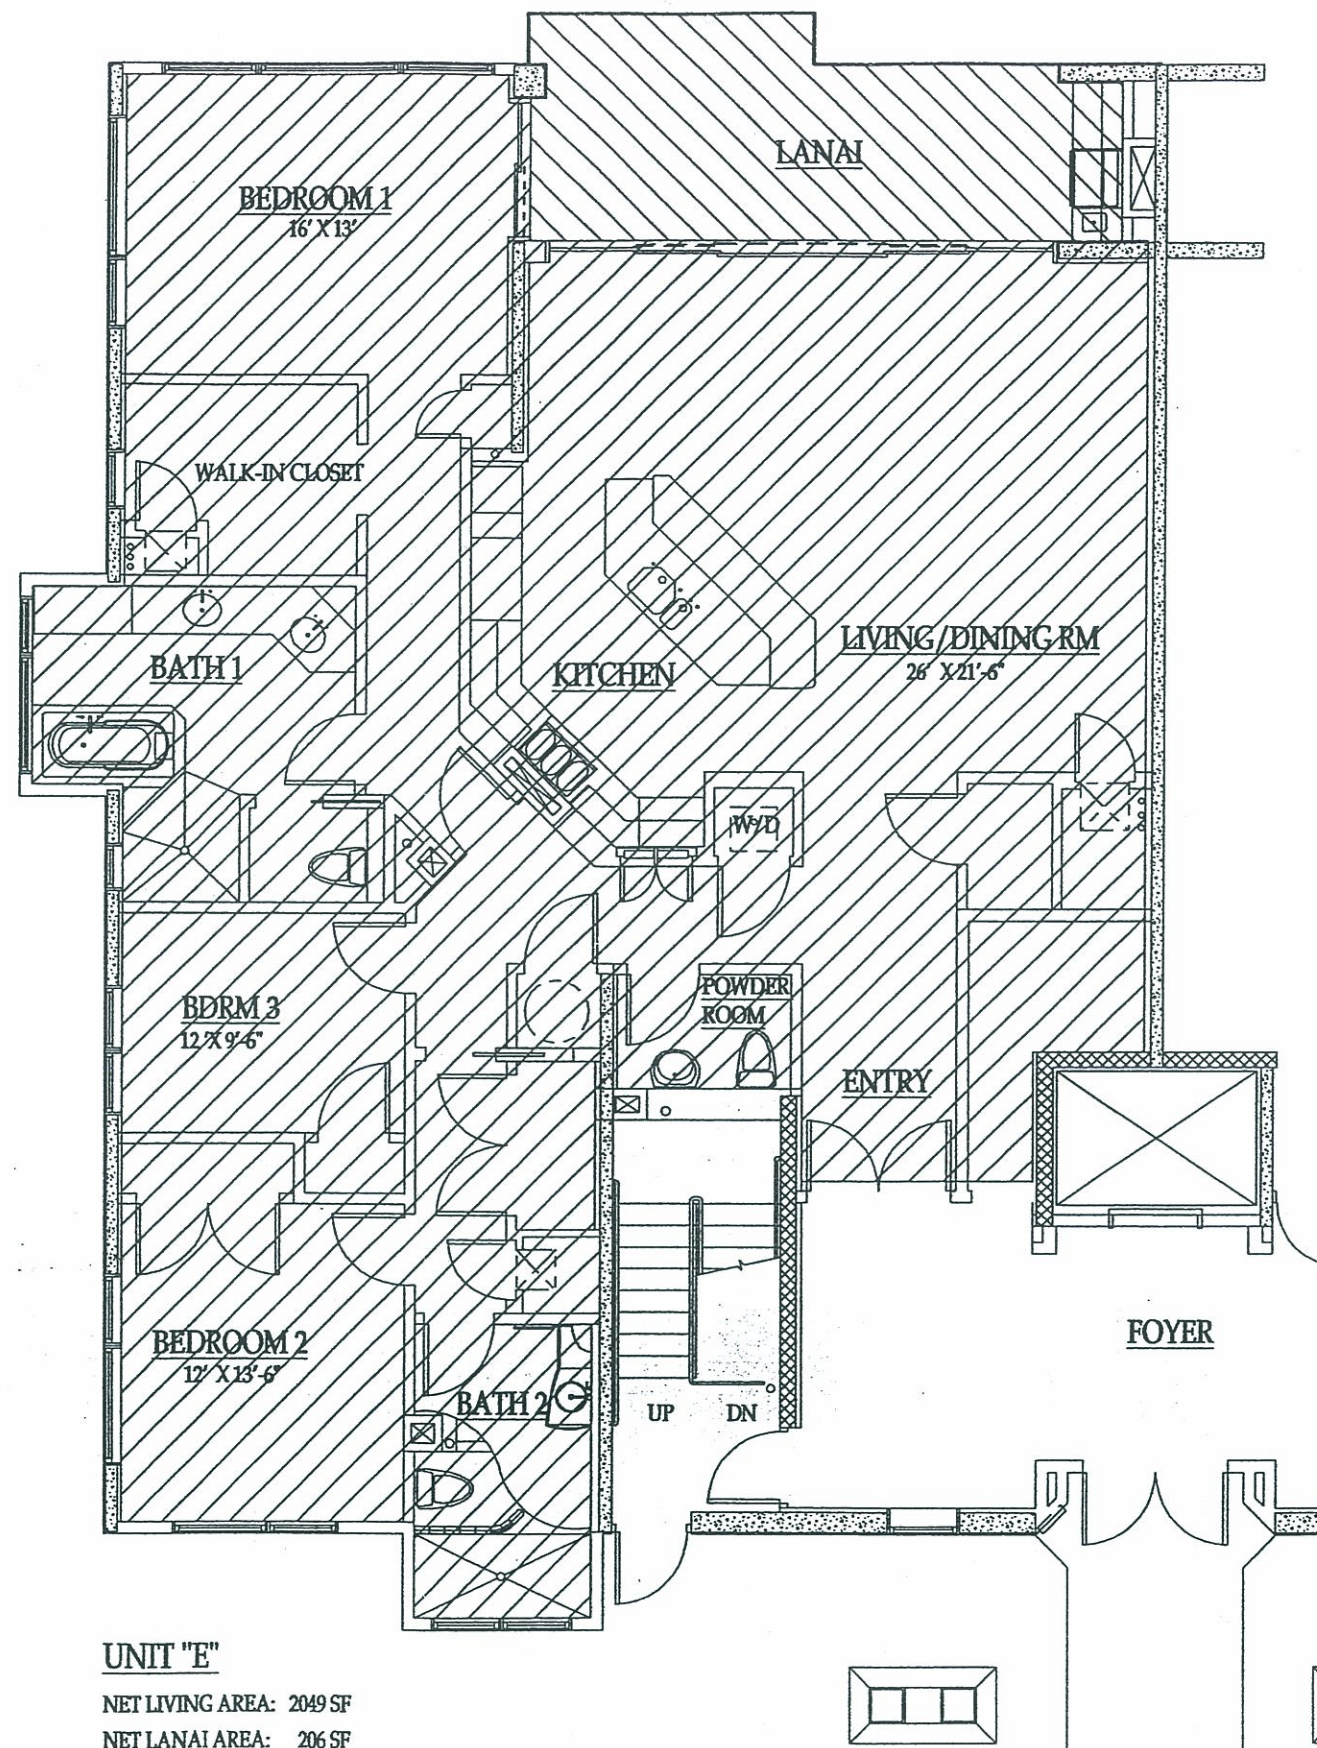

UNIT "E"

NET LIVING AREA: 2049 SF

NET LANAI AREA: 206 SF

3 Bedroom
Ground Floor


SCALE: 1/8" = 1'-0"

Makena Estates, LLC



FIRST AMENDED CONDOMINIUM MAP

Nā Hale  Mākena
M ā k e n a , M a u i , H a w a i ' i

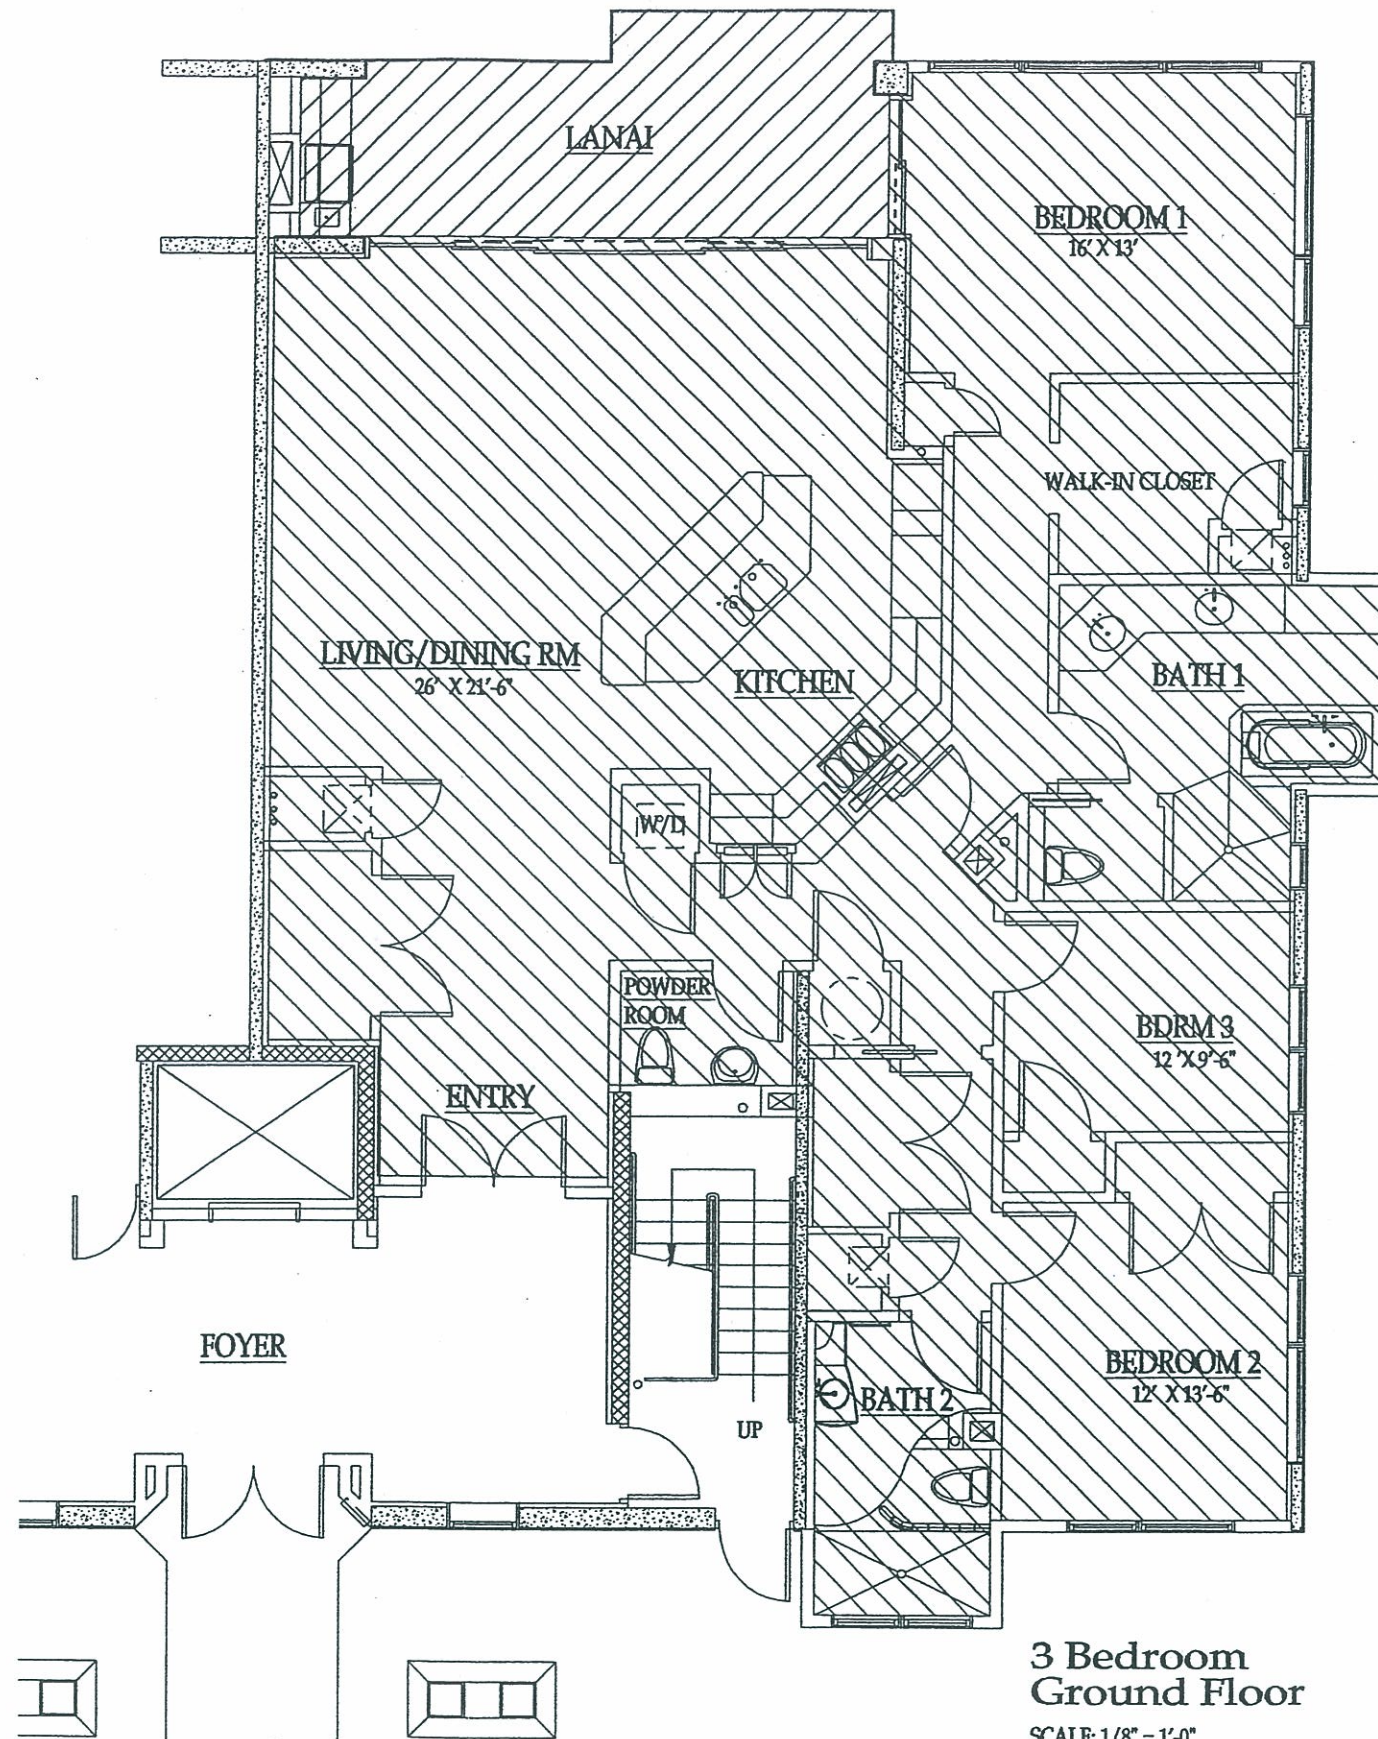

UNIT "F"
 NET LIVING AREA: 2116 SF
 NET LANAI AREA: 206 SF


3 Bedroom
 Ground Floor
 SCALE: 1/8" = 1'-0"

Makena Estates, LLC



FIRST AMENDED CONDOMINIUM MAP

Nā Hale  Mākena
 M ā k e n a , M a u i , H a w a i ' i

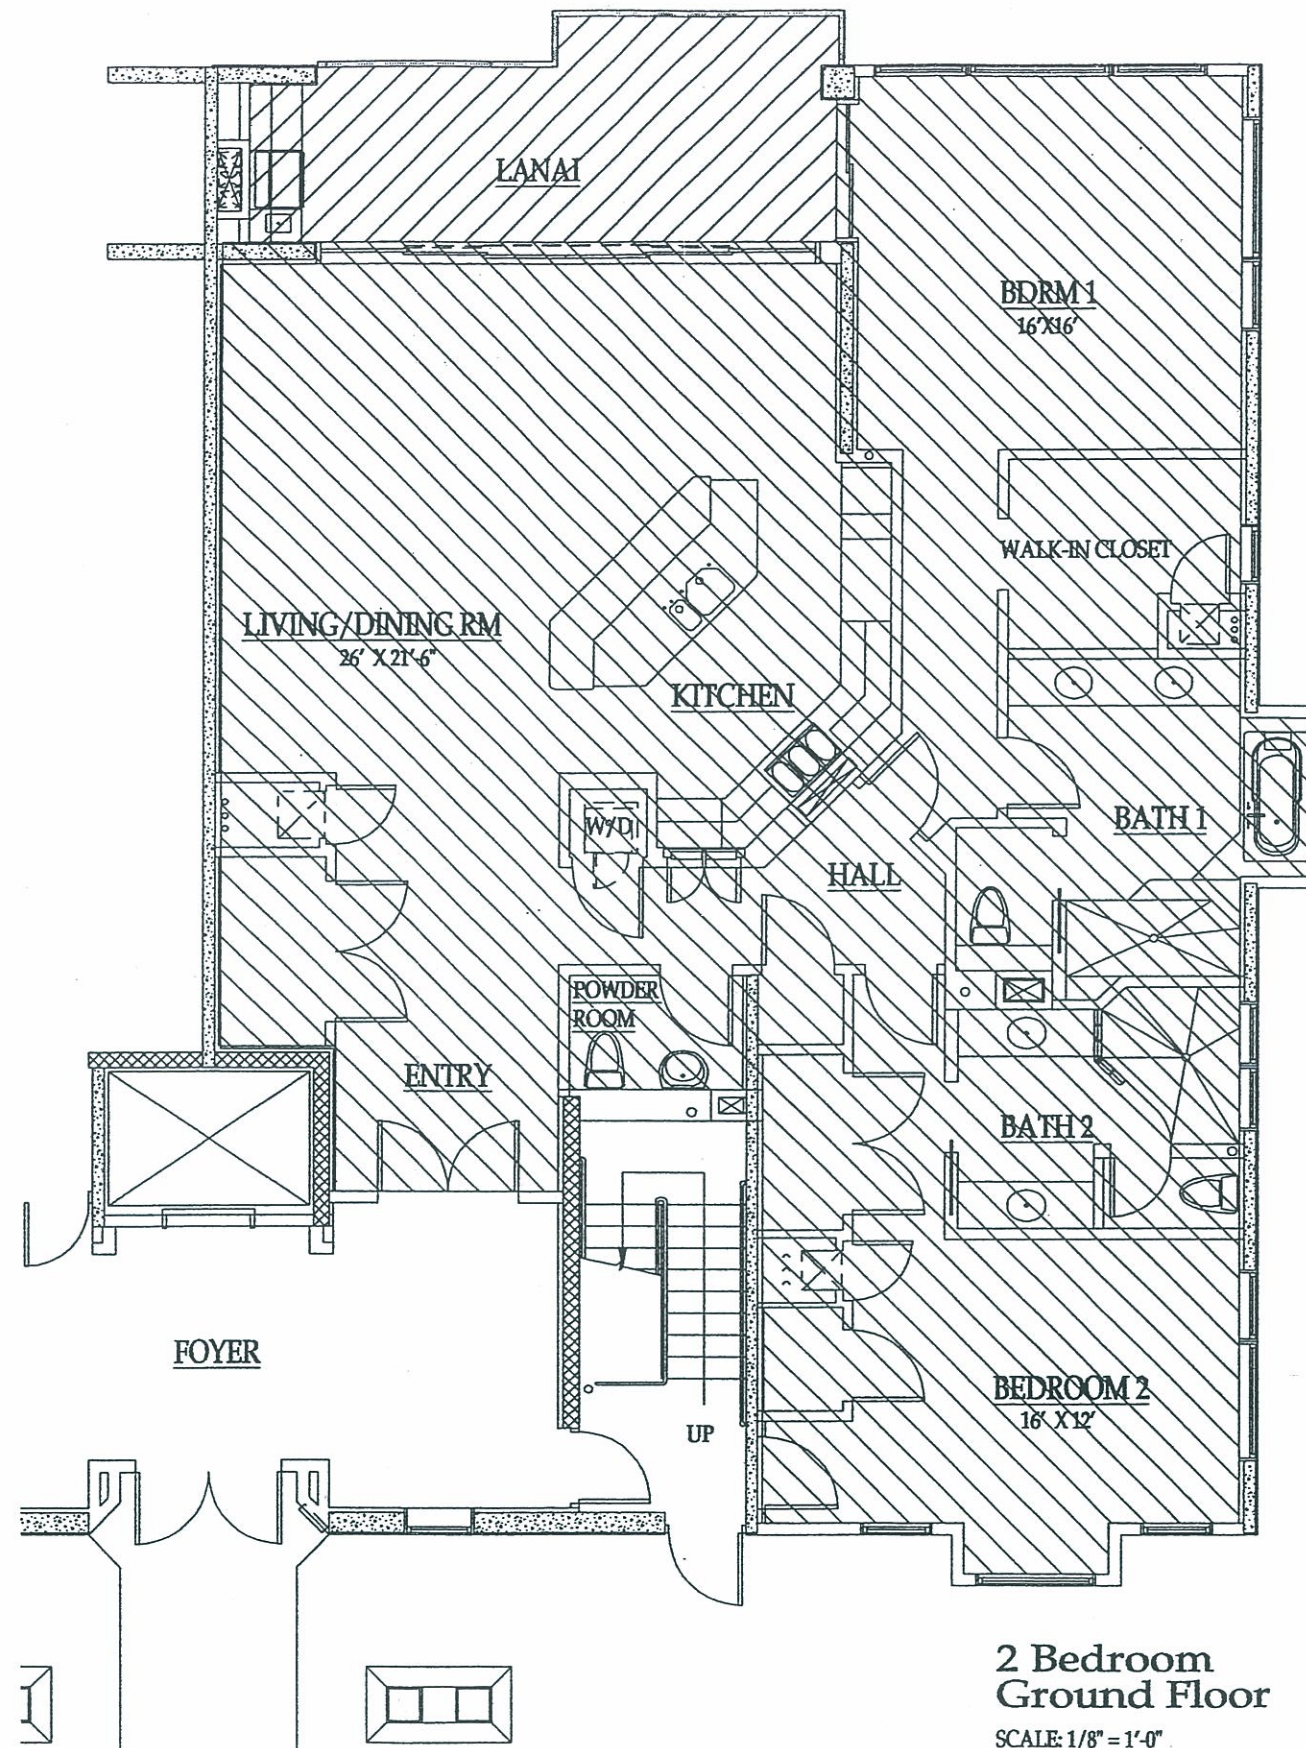

UNIT "G"

NET LIVING AREA: 2088 SF

NET LANAI AREA: 206 SF

2 Bedroom
Ground Floor

SCALE: 1/8" = 1'-0"

FIRST AMENDED CONDOMINIUM MAP

Makena Estates, LLC




Nā Hale  Mākena
M ā k e n a , M a u i , H a w a i ' i



FRONT ELEVATION



RIGHT ELEVATION

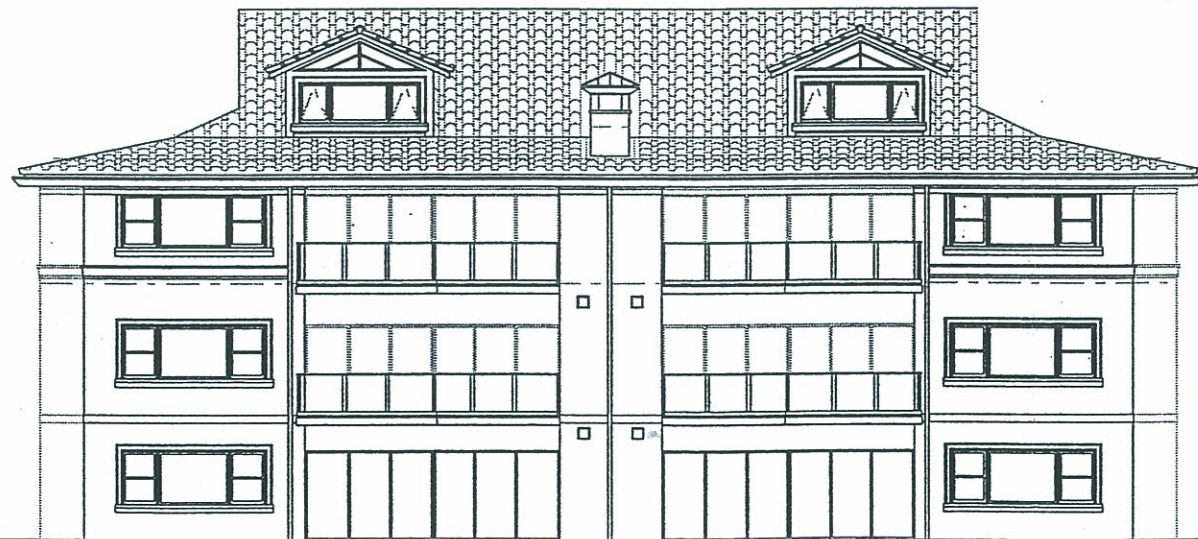

REAR ELEVATION



LEFT ELEVATION

Makena Estates, LLC



FIRST AMENDED CONDOMINIUM MAP

Nā Hale  Mākena
M ā k e n a, M a u i, H a w a i ' i




ELEVATIONS - 3 STORY
BUILDING A & D



FRONT ELEVATION



RIGHT ELEVATION

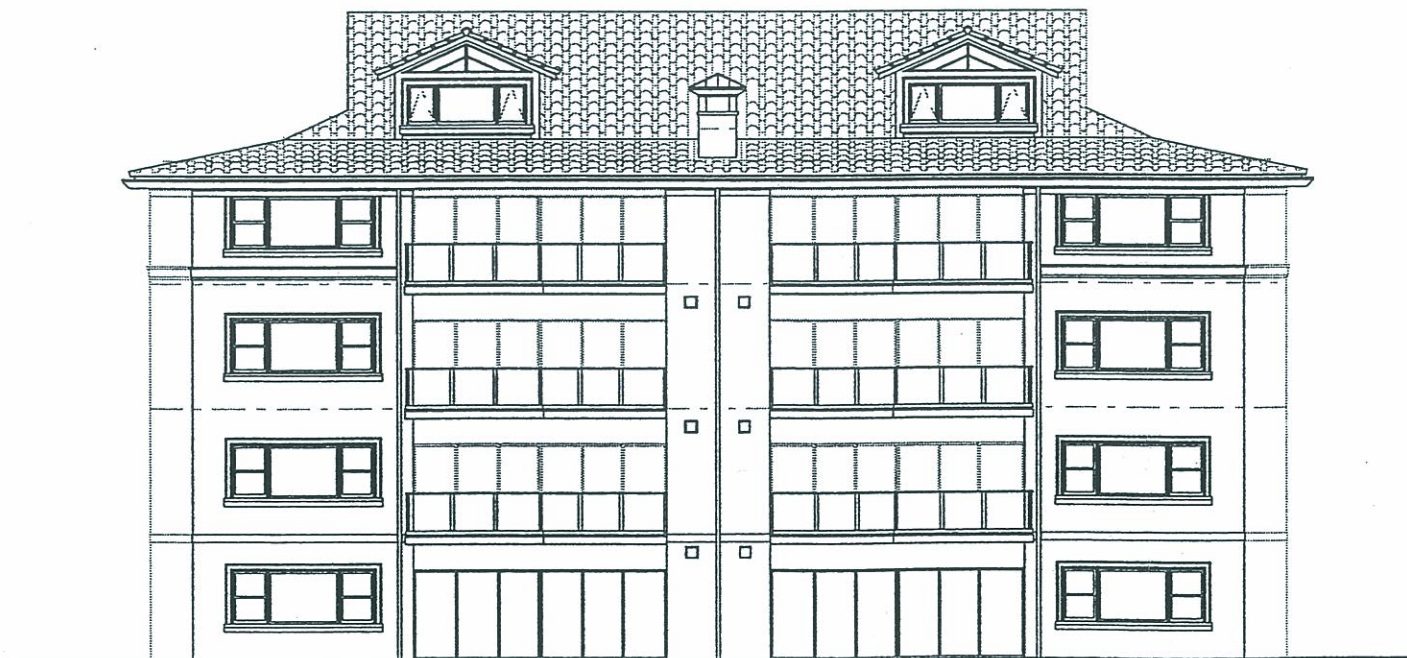

REAR ELEVATION



LEFT ELEVATION

Makena Estates, LLC




FIRST AMENDED CONDOMINIUM MAP

Nā Hale  Mākena
M ā k e n a, M a u i, H a w a i ' i




ELEVATIONS-4STORY
BUILDING B&C

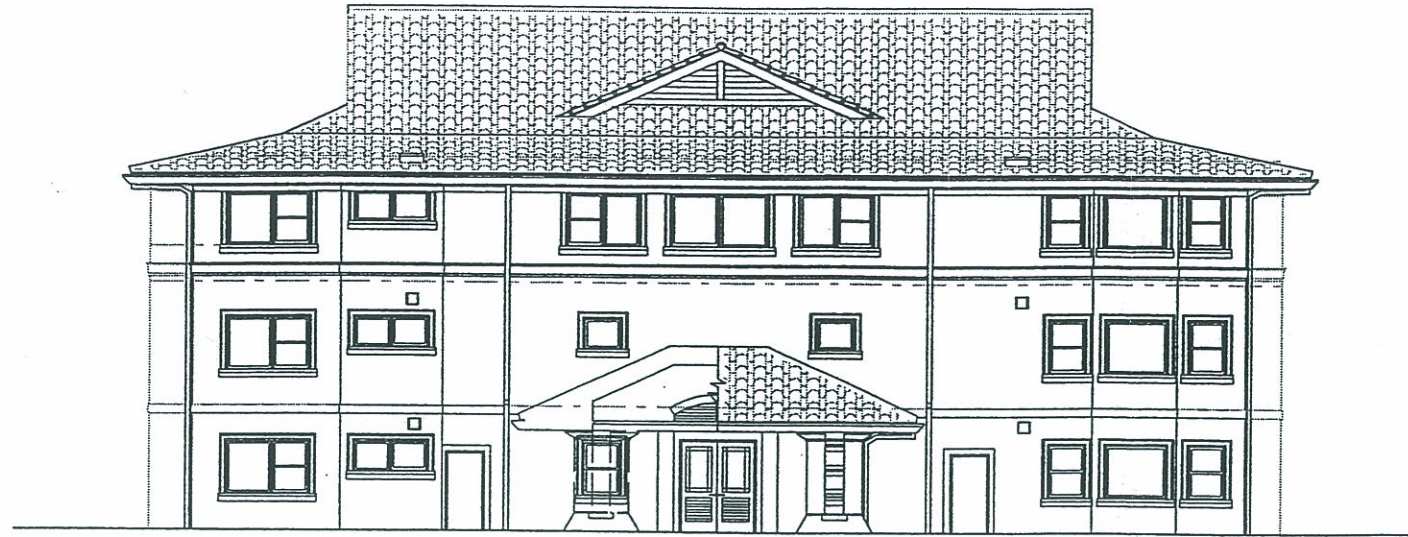

FRONT ELEVATION



RIGHT ELEVATION

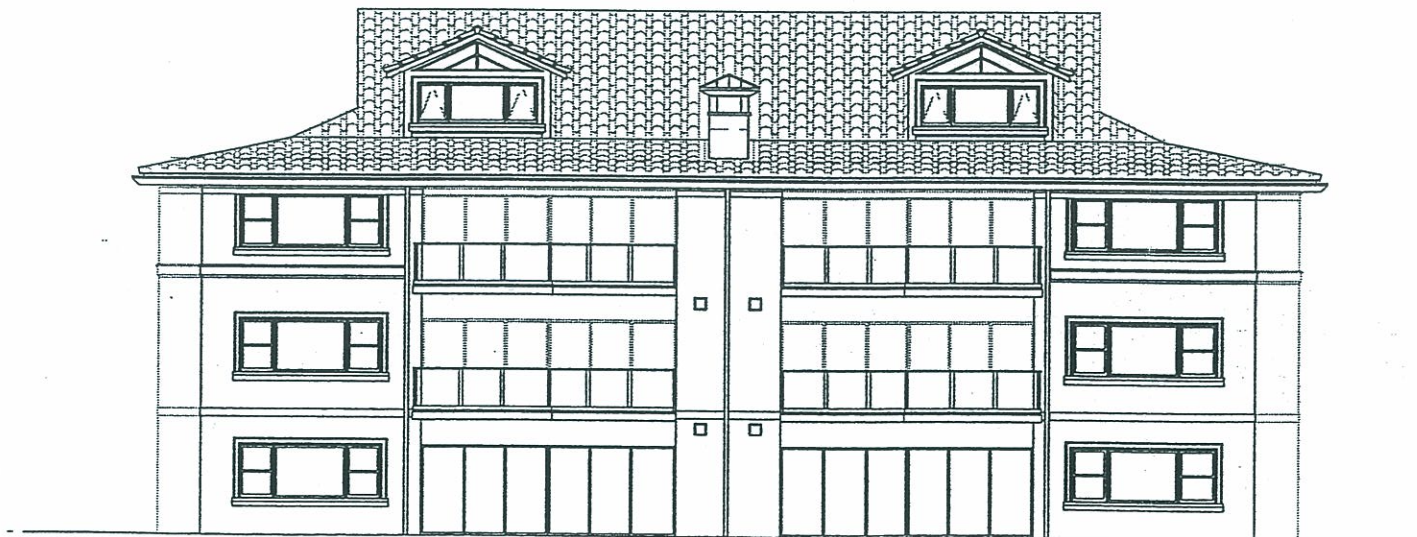

REAR ELEVATION



LEFT ELEVATION

Makena Estates, LLC




FIRST AMENDED CONDOMINIUM MAP


Nā Hale Mākena
Mākena, Maui, Hawai'i




ELEVATIONS - 3 STORY
BUILDING E&F

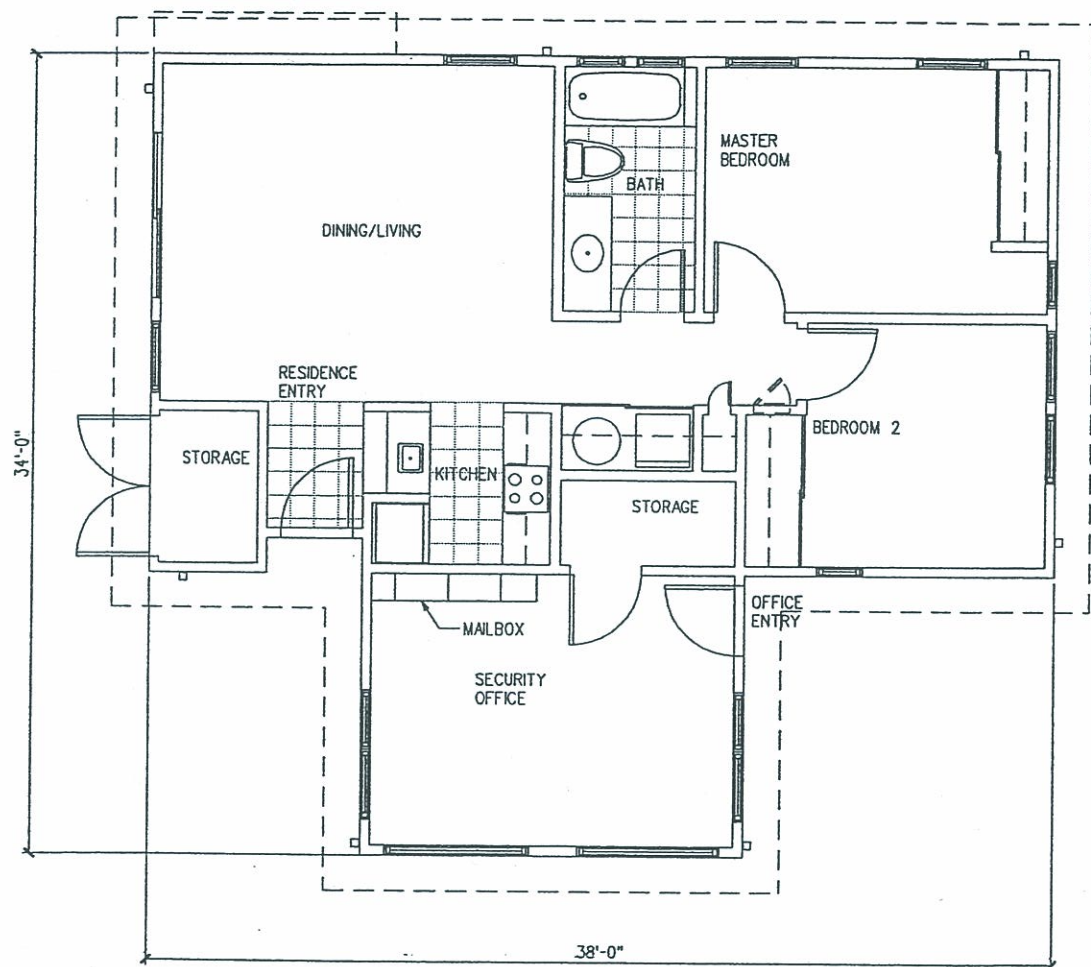


FLOOR PLAN
0 4' 8'

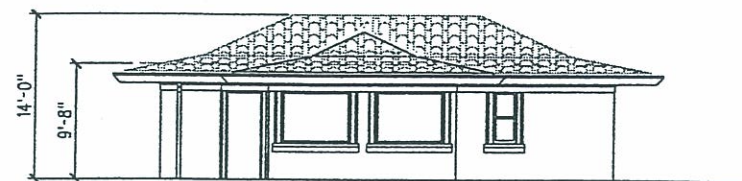


FRONT ELEVATION

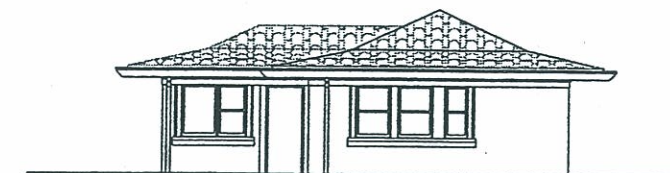

RIGHT ELEVATION

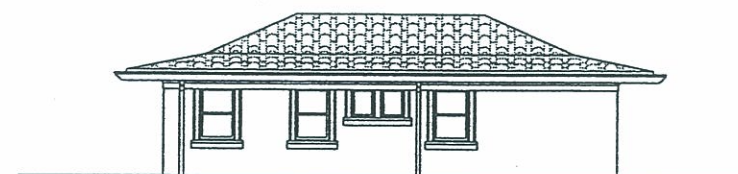

REAR ELEVATION

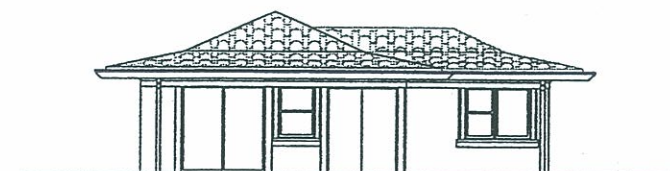

LEFT ELEVATION

EXTERIOR ELEVATIONS
0 8' 16'


Makena Estates, LLC



FIRST AMENDED CONDOMINIUM MAP

RESIDENCE MANAGER'S UNIT

Nā Hale  Mākena
M ā k e n a, M a u i, H a w a i ' i

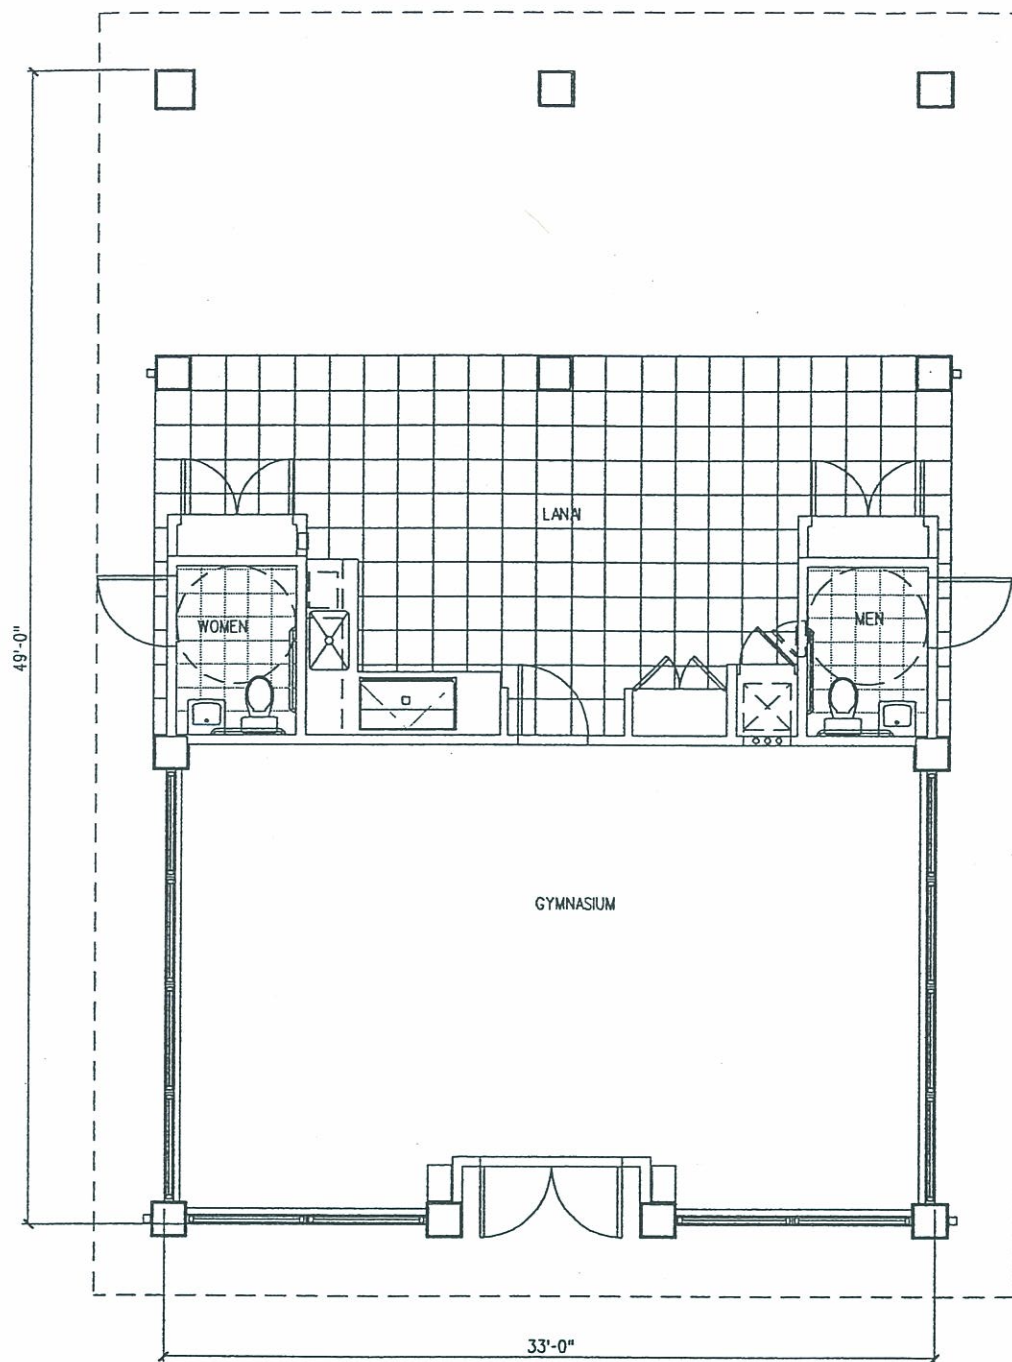


FLOOR PLAN


0 4' 8'




FRONT ELEVATION

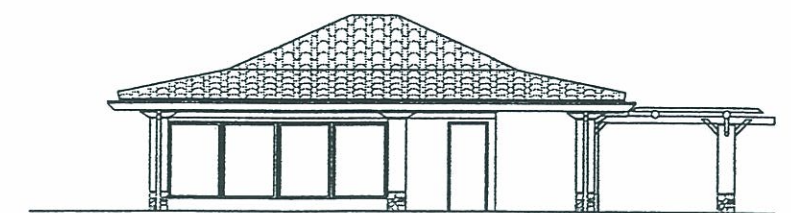

RIGHT ELEVATION

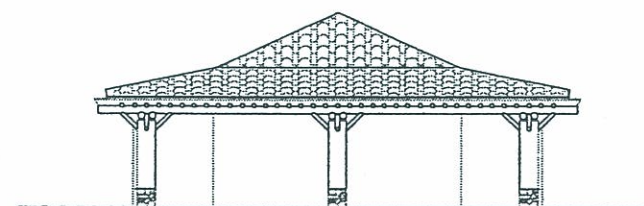

REAR ELEVATION

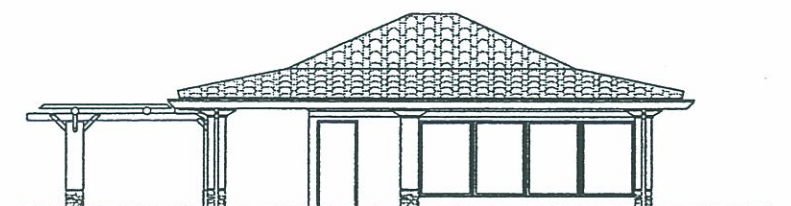

LEFT ELEVATION

EXTERIOR ELEVATIONS

0 8' 16'

Makena Estates, LLC



FIRST AMENDED CONDOMINIUM MAP

RECREATION CABANA

Nā Hale  Mākena
M ā k e n a, M a u i, H a w a i ' i